

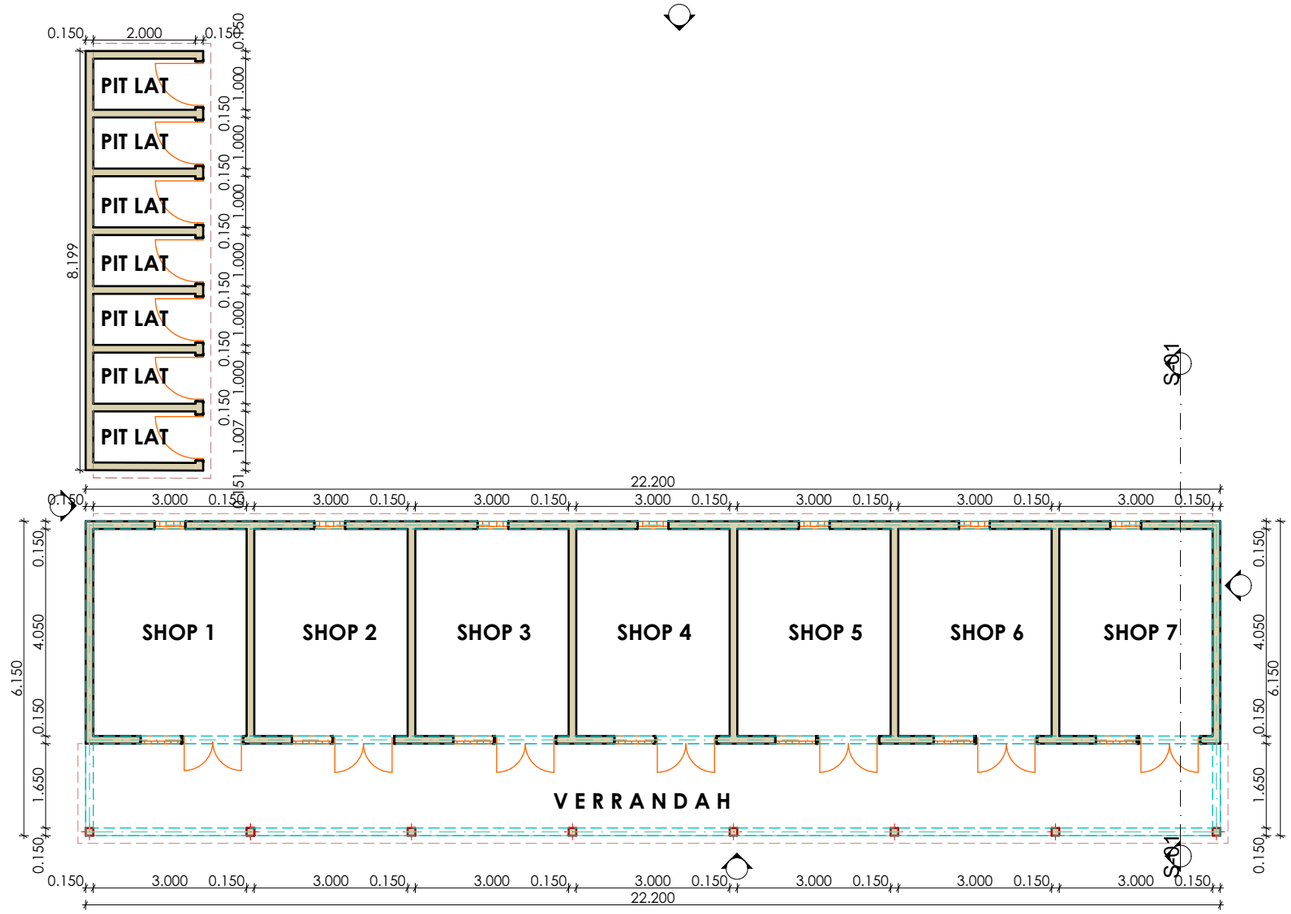



0. Ground Floor 1:120

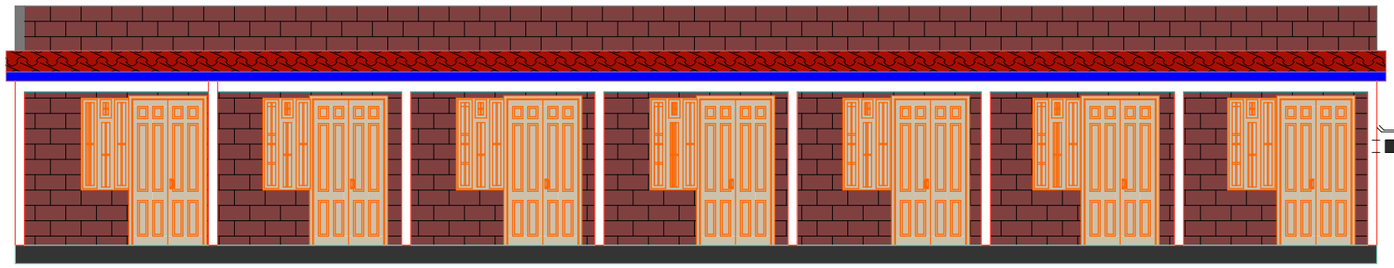


Elevation 1 1:100

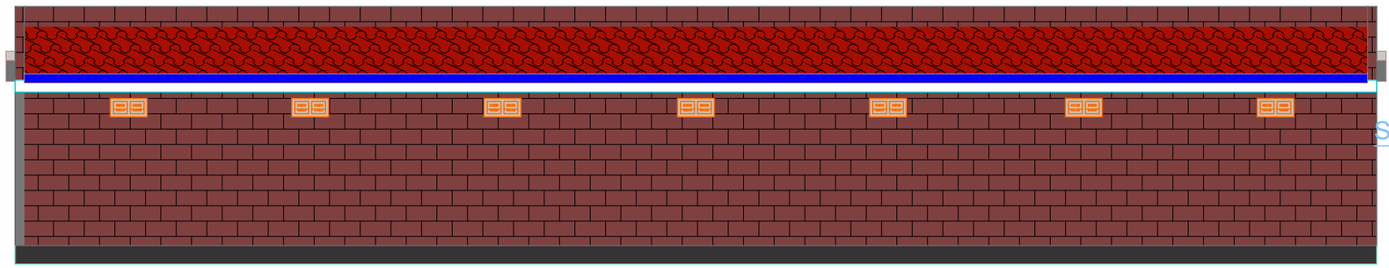



Elevation 2 1:100

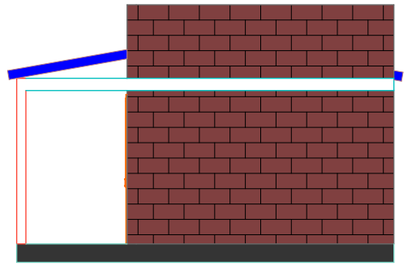

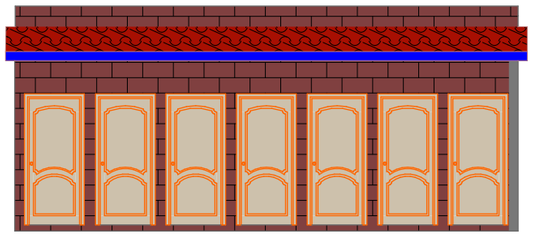


Elevation 3 1:100

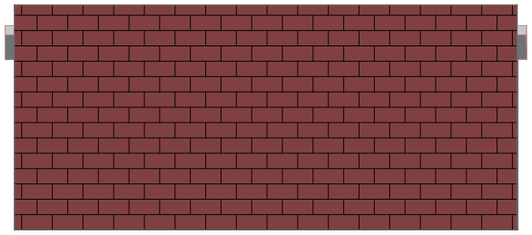

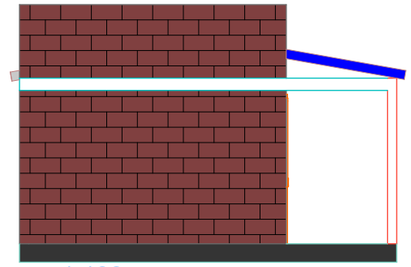

Elevation 4 1:100

Roof details
Roof pitch 10 degrees
Approved gauge metal sheeting on
75x50mm purlins
100x50mm struts & ties
100x50mm rafters ties beams and king post
50x50mm ceiling brandering binded with
100x25mm moulded cornice
200x50m fascia board painted to approval

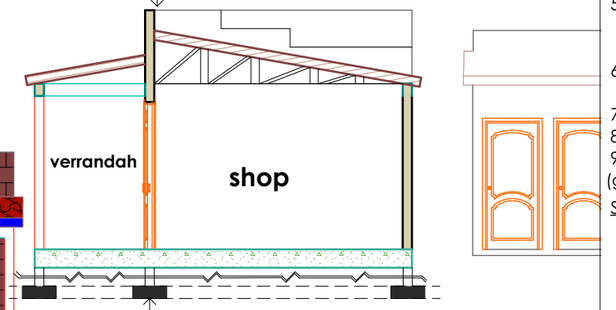

Foundation details
25mm screed
100mm thick reinforced concrete slab
500gauge dpm sheet
300mm thick well compacted hardcore
600x200mm strip foundation
N/B provide for anti-termite treatment
(gladiator or any other approved pesticide)

S-01 Building Section 1:100

NOTES

GENERAL NOTES
1. All dimensions are in meters unless otherwise specified
2. All dimensions to be checked on site and any discrepancies referred to the architect
3. Drawings are not to be scaled, only figured dimensions to be used
4. Dimensions are to be read out and not measured
5. The contractor must check and verify all dimensions on site before commencing any work
6. Concrete 1:2:4 three quater grade and to be according to general specifications
7. Reinforcement mild steel to be BS 785.
8. Cover to reinforcement bays to be 25mm.
9. Provide for anti-termite treatment (gladiator or any other approved pesticide)

STRUCTURAL
10. For all RC works,refer to the structural engineer's details
11. Depth of the foundation to be determained on site to structural engineer's approval
12. Walls to be reinforced with hoop iron at every alternate course
13. All adjacent RC works and masonry walls to be tied with strap iron at every course
14. Clay soil to be removed on site before commencement of the construction.

PROJECT:
PROPOSED COMMERCIAL DEVELOPMENT ON PLOT LR.

CLIENT:
CONTACT:

DRAWN BY: MARTIN (0748140132)
APPROVED BY:
SIGNATURE **DATE**

DRAWING TITLE.
1.Floor plan
2. Section
3.Elevation(Elevation 1, Elevation 2, Elevation 3, Elevation 4)
4.Details

Drawing Scale 1:120, 1:100
DATE: 28/08/2026